
SUPPLY SCOPE: only the Nudura ICF formwork and associated accessories are in our price. Slab, floor, roof, joinery, Dryvit render, tapes, roofing and stair are supplied in good faith from the model and must be checked by the relevant professional. PERMITTED DEVELOPMENT (Class E): eaves 2473 < 2,500, ridge 3949 < 4,000 - check the 2 m boundary rule (2.5 m cap). Loft = storage.

QUOTATION - NOT FOR CONSTRUCTION

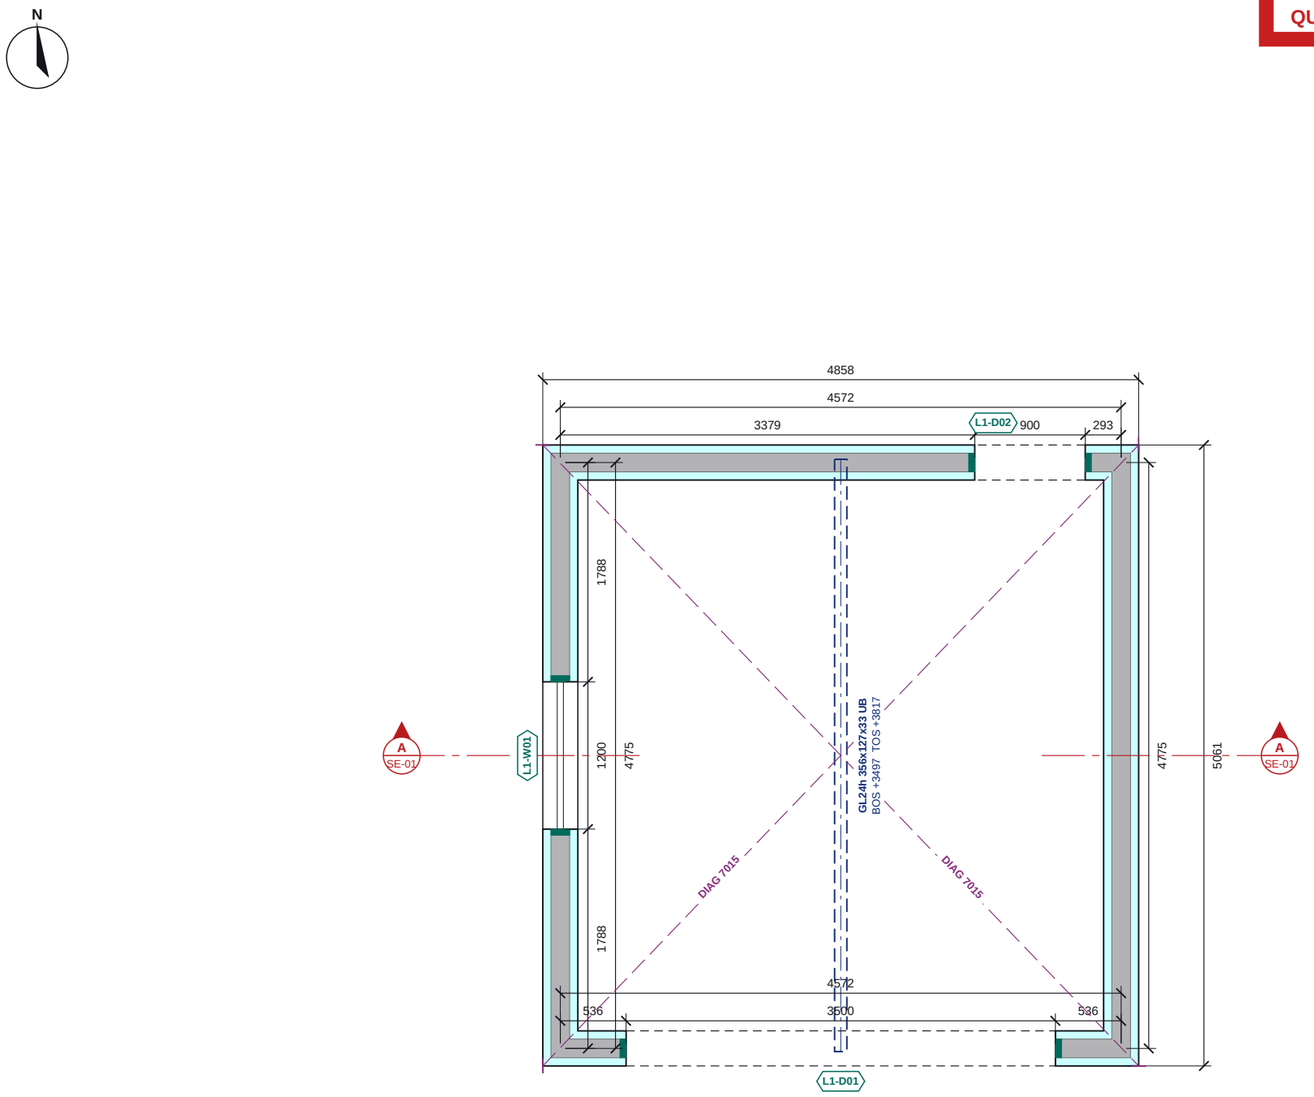

EPS insulation (Nudura form)
Concrete core
End cap at opening
Steel over (dashed), marked
Engineer's pier bars (n-H12 vertical bars in ICF pier) / WS wall starters
Setting-out check diagonal (external ICF corners)
Section line (see SE sheet)

GROUND FLOOR ICF PLAN

Scale 1:50 @ A3 | Plan cut at 1200 above GF FFL

0 1 2 3m

Do not scale. All dimensions in millimetres, levels in metres from GF FFL. Check all dimensions on site.

GROUND FLOOR ICF SCHEDULES

OPENING SCHEDULE

Ref	Width	Height	Sill	Head	Lintel
L1-D01	3500	2286	0	+2286	-
L1-D02	900	2100	0	+2100	-
L1-W01	1200	900	+1000	+1900	-

Structural openings in the ICF; sill and head above GF FFL.

STEEL SCHEDULE

Mark	Section (engineer)	BOS	TOS
GL24h	356x127x33 UB S355	+3497	+3817

BOS / TOS = bottom / top of steel above GF FFL (C-1 columns: base / top).

NOTES

1. ICF: Nudura 6" Std, 66.7 EPS + 152.4 core + 66.7 EPS = 285.8. Dimensions to the ICF faces.
2. Levels above GF FFL. Sill / head = structural opening in the ICF.
3. No structural design yet. ICF per the quotation model: Nudura 6in Standard, 3,500 x 2,286 garage door with a one-course lintel under the raked gable glazing, glulam ridge bearing in the gables, raft slab - engineer to design.
4. Lintel (L-n) and steel (B-n, C-1) marks from rev -, which takes precedence.
5. Masonry walls shown for context.
6. Steel over dashed. BOS / TOS = bottom / top of steel above GF FFL.
7. Datum: 0 = raft slab top / garage floor. Replacement for the 4,950 x 5,110 precast double garage (site address TBC).

REVISIONS

REV	DATE	DESCRIPTION
Q01	28.10.26	First issue

Nudura™ BuildEase

CLIENT	PROJECT
Dortech Direct (James, MD) via Andy Claridge, Tremco CPG	Two-storey garage in Nudura ICF - Option A - Permitted Development

DRAWING TITLE

GARAGE ICF GENERAL ARRANGEMENT

ICF walls, openings, lintels, steel over and engineer's notes

SCALE	SIZE	DATE
1:50	A3	28.10.26
DRAWN	CHECKED	APPROVED
TS		

STATUS	DRAWING No.	REV
QUOTATION	DG-A-GA-01	Q01