
**SUPPLY SCOPE: only the Nudura ICF formwork and associated accessories are in our price. Slab, floor, roof, joinery, Dryvit render, tapes, roofing and stair are supplied in good faith from the model and must be checked by the relevant professional. PERMITTED DEVELOPMENT (Class E): eaves 2473 < 2,500, ridge 3949 < 4,000 - check the 2 m boundary rule (2.5 m cap). Loft = storage.**

**QUOTATION - NOT FOR CONSTRUCTION**

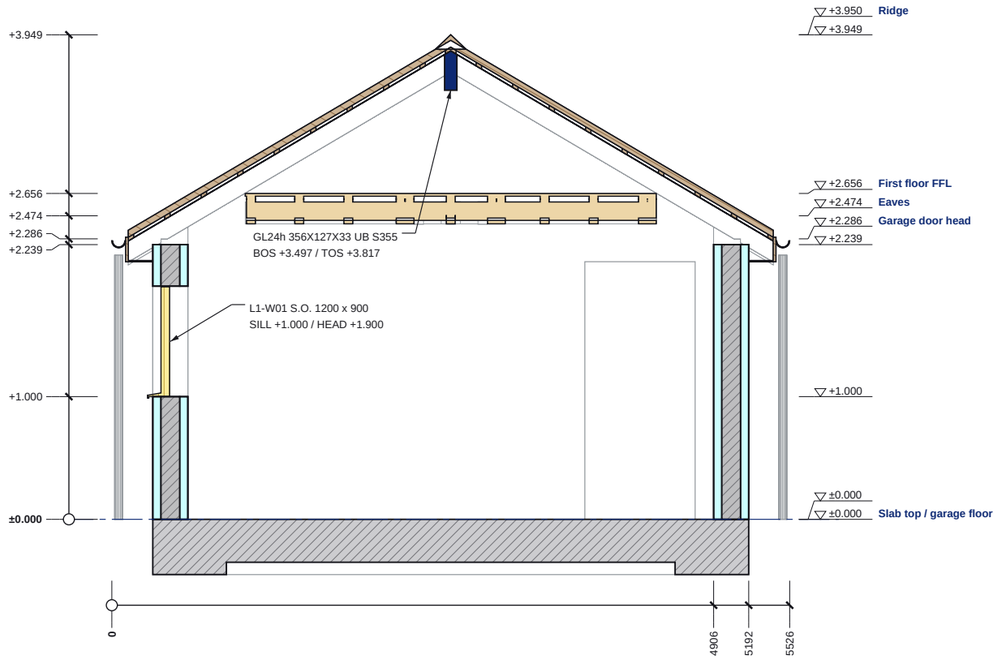


## SECTION A-A

Scale 1:50 @ A3 | Looking north; levels above GF FFL

ICF EPS (cut)
ICF concrete core / RC (cut)
Steel (cut)
Beyond the cut (line work)

0 1 2m

## SECTION A-A SCHEDULES


### LEVELS ON THIS SECTION

| Level | FFL |
|---|---|
| Slab top / garage floor | ±0.000 |
| top of ICF W01 | +1.000 |
| top of ICF W03 | +2.239 |
| Garage door head | +2.286 |
| Eaves | +2.474 |
| First floor FFL | +2.656 |
| top of roof build-up | +3.949 |
| Ridge | +3.950 |

### STEEL CUT BY THIS SECTION

| Mark | Section (engineer) | BOS | TOS |
|---|---|---|---|
| GL24h | 356x127x33 UB S355 | +3.497 | +3.817 |

### SECTION KEY

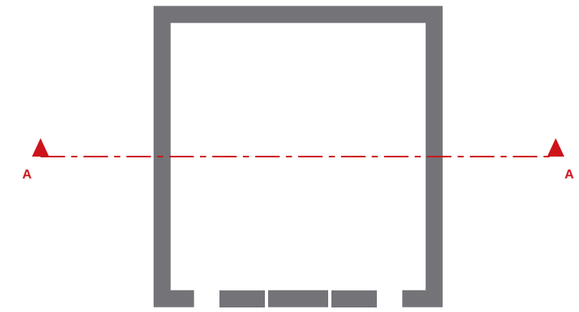


### NOTES

1. Section A-A is a BuildEase ICF section (not an architect's section line). Cut elements hatched / filled; the model beyond the cut in line work.
2. Levels above GF FFL.
3. ICF: Nudura 6" Std, 66.7 EPS + 152.4 core + 66.7 EPS = 285.8, 152.4 core + 66.7 EPS = 285.8. No structural design yet. ICF per the quotation model: Nudura 6in Standard, 3,500 x 2,286 garage door with a one-course lintel under the raked gable glazing, glulam ridge bearing in the gables, raft slab - engineer to design.
4. Steel marks, BOS / TOS: rev -. See DG-A-GA-01 / EL-01 / EL-02 in the approval drawings pack.
5. Datum: 0 = raft slab top / garage floor. Replacement for the 4,950 x 5,110 precast double garage (site address TBC).

### REVISIONS

| REV | DATE | DESCRIPTION |
|---|---|---|
| Q01 | 28.10.26 | First issue |

Nudura™ BuildEase

| CLIENT | PROJECT |
|---|---|
| Dortech Direct (James, MD) via Andy Claridge, Tremco CPG | Two-storey garage in Nudura ICF - Option A - Permitted Development |

DRAWING TITLE
**SECTION A-A**
ICF section with levels and build-ups

| SCALE | SIZE | DATE |
|---|---|---|
| 1:50 | A3 | 28.10.26 |
| DRAWN | CHECKED | APPROVED |
| TS | | |

| STATUS | DRAWING No. | REV |
|---|---|---|
| QUOTATION | DG-A-SE-01 | Q01 |

Do not scale. All dimensions in millimetres, levels in metres from GF FFL. Check all dimensions on site.