
SUPPLY SCOPE: only the Nudura ICF formwork and associated accessories are in our price. Slab, floor, roof, joinery, Dryvit render, tapes, roofing and stair are supplied in good faith from the model and must be checked by the relevant professional. PLANNING APPLICATION: ridge 5988 is above the Class E 4.0 m limit; eaves 2474 kept < 2,500. Room in the roof by an external steel stair.

QUOTATION - NOT FOR CONSTRUCTION

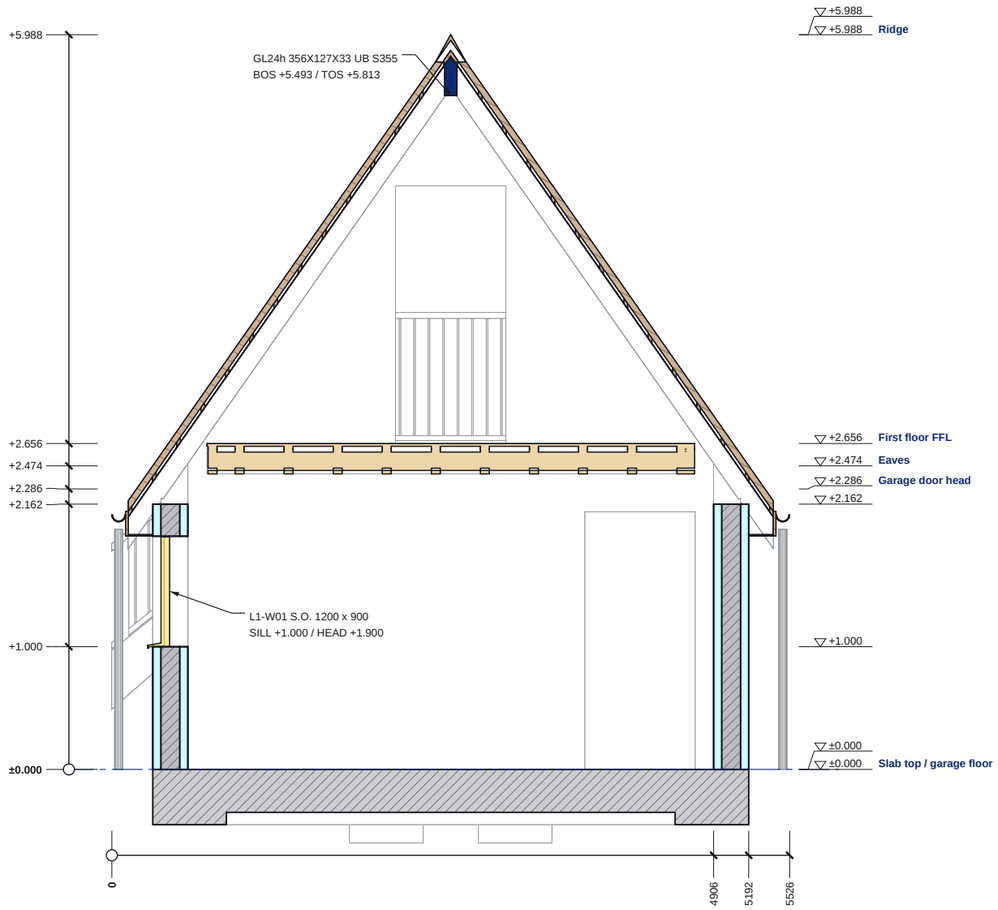

SECTION A-A

Scale 1:50 @ A3 | Looking north; levels above GF FFL

ICF EPS (cut)
ICF concrete core / RC (cut)
Steel (cut)
Beyond the cut (line work)

0 1 2m

SECTION A-A SCHEDULES


LEVELS ON THIS SECTION

Level	FFL
Slab top / garage floor	±0.000
top of ICF W01	+1.000
top of ICF W03	+2.162
Garage door head	+2.286
Eaves	+2.474
First floor FFL	+2.656
Ridge	+5.988

STEEL CUT BY THIS SECTION

Mark	Section (engineer)	BOS	TOS
GL24h	356x127x33 UB S355	+5.493	+5.813

SECTION KEY

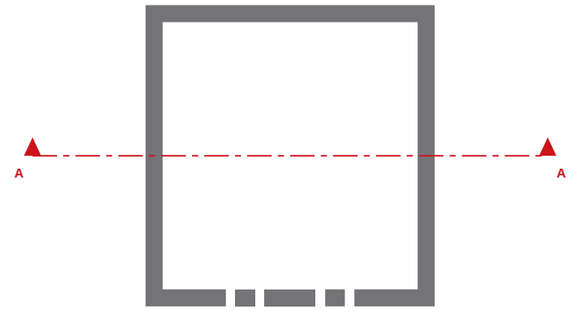

NOTES

1. Section A-A is a BuildEase ICF section (not an architect's section line). Cut elements hatched / filled; the model beyond the cut in line work.
2. Levels above GF FFL.
3. ICF: Nudura 6" Std, 66.7 EPS + 152.4 core + 66.7 EPS = 285.8, 152.4 core + 66.7 EPS = 285.8. No structural design yet. ICF per the quotation model: Nudura 6in Standard, 3,500 x 2,286 garage door with a one-course lintel under the raked gable glazing, glulam ridge bearing in the gables, raft slab - engineer to design.
4. Steel marks, BOS / TOS: rev -. See DG-B-GA-01 / EL-01 / EL-02 in the approval drawings pack.
5. Datum: 0 = raft slab top / garage floor. Replacement for the 4,950 x 5,110 precast double garage (site address TBC).

REVISIONS

REV	DATE	DESCRIPTION
Q01	28.10.26	First issue

Nudura™ BuildEase

CLIENT	PROJECT
Dortech Direct (James, MD) via Andy Claridge, Tremco CPG	Two-storey garage in Nudura ICF - Option B - Room in the roof

DRAWING TITLE
SECTION A-A
ICF section with levels and build-ups

SCALE	SIZE	DATE
1:50	A3	28.10.26
DRAWN	CHECKED	APPROVED
TS		

STATUS	DRAWING No.	REV
QUOTATION	DG-B-SE-01	Q01

Do not scale. All dimensions in millimetres, levels in metres from GF FFL. Check all dimensions on site.